


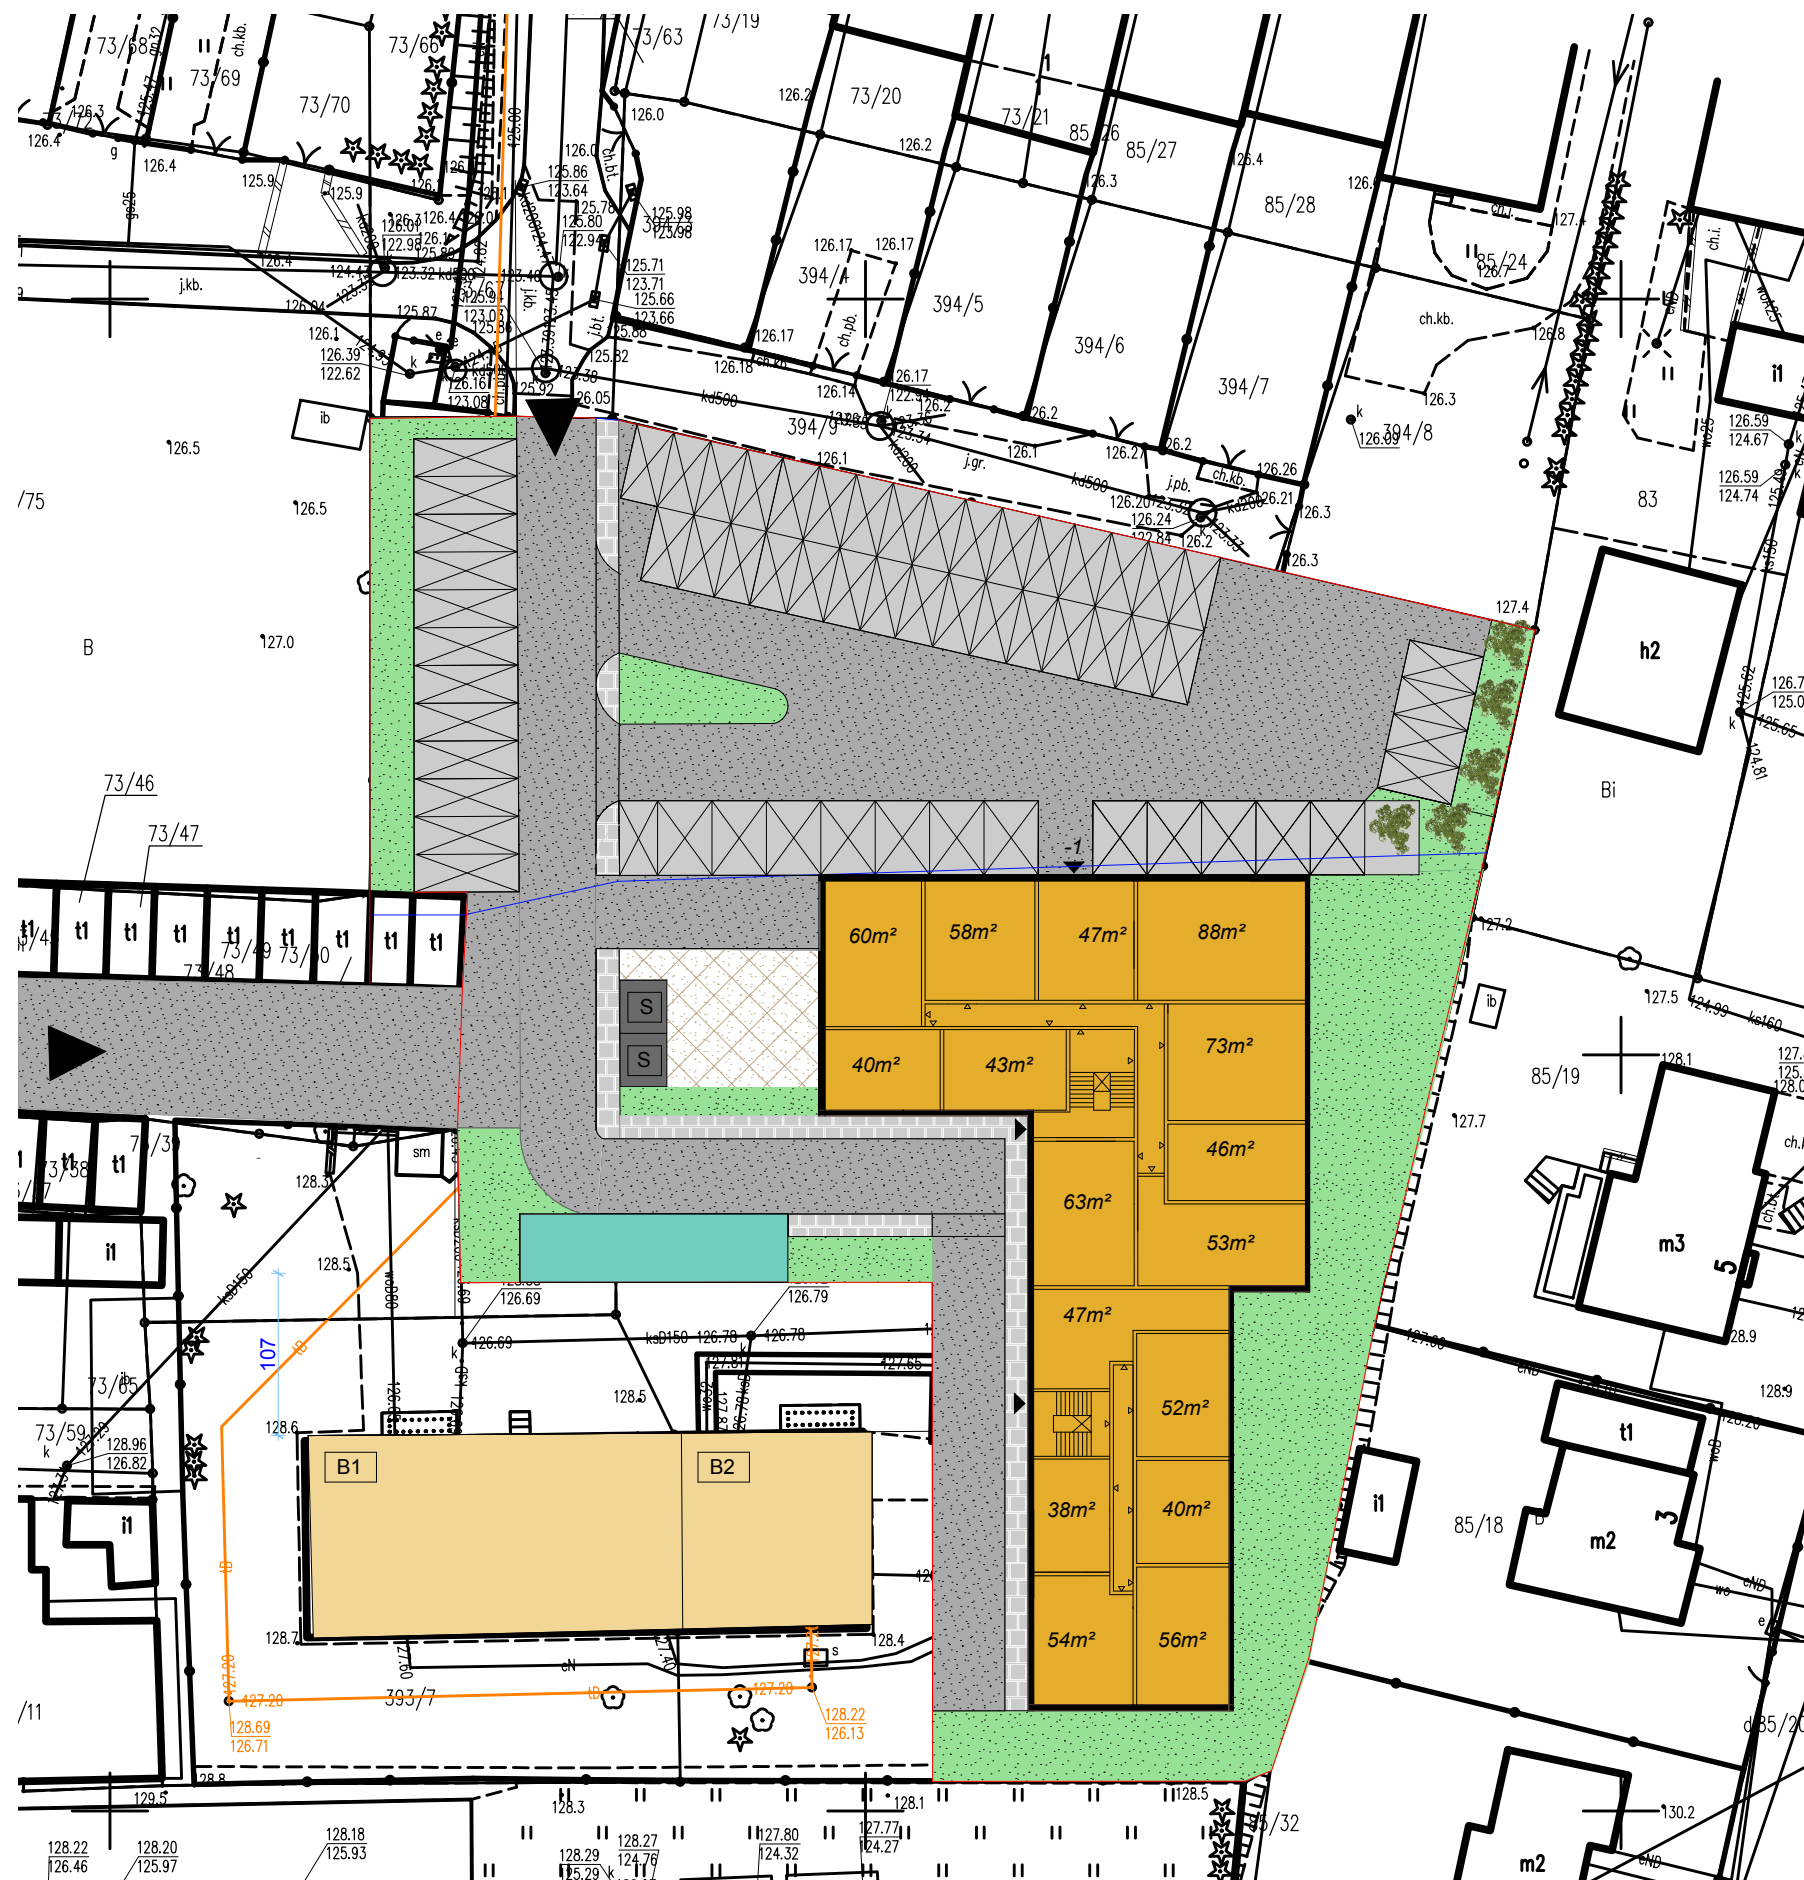

## RZUT PARTERU

- ZAKRES INWESTYCJI
- LINIA ROZGRANICZAJĄCA TERENY MPZP
- BW PROJEKTOWANY BUDYNEK WIELORODZINNY 5-KONDYGNACYJNY+GARAŻ PODZIEMNY
- B1 B2 ISTNIEJĄCE BUDYNKI WIELORODZINNE
- PZ PLAC ZABAW, TEREN REKREACYJNY
- S LOKALIZACJA ŚMIETNIKA
- POWIERZCHNIA BIOLOGICZNIE CZYNNNA
- DOJAZDY-KOMUNIKACJA KOŁOWA
- MIEJSCA POSTOJOWE-PARKINGI
- DOJŚCIA-KOMUNIKACJA PIESZA
- TEREN WYŁĄCZONY
- WJAZD NA DZIAŁKĘ
- PROJEKTOWANA ZIELEŃ
- WEJŚCIA DO BUDYNKU

### BILANS POWIERZCHNI:

|                                                                 |                       |
|-----------------------------------------------------------------|-----------------------|
| • POWIERZCHNIA ZABUDOWY                                         | 1112,04m <sup>2</sup> |
| • POWIERZCHNIA UŻYTKOWA MIESZKAŃ -DOT.1 KONDYGNACJI             | 858,00m <sup>2</sup>  |
| • POWIERZCHNIA UŻYTKOWA MIESZKAŃ -DOT.WSZYSTKICH KONDYGNACJI    | 4290,00m <sup>2</sup> |
| • POWIERZCHNIA CAŁKOWITA KONDYGNACJI NAZIEMNYCH                 | 4870,30m <sup>2</sup> |
| • POWIERZCHNIA KOMUNIKACJI (klatka+korytarz) DOT. 1 KONDYGNACJI | 116,06m <sup>2</sup>  |
| • POWIERZCHNIA KOMUNIKACJI DOT.WSZYSTKICH KONDYGNACJI           | 580,30m <sup>2</sup>  |
| • ILOŚĆ MIESZKAŃ NA 1 KONDYGNACJI                               | 16szt                 |
| • CHARAKTERYSTYKA MIESZKAŃ:                                     |                       |
| - ILOŚĆ MIESZKAŃ 38m <sup>2</sup> -47m <sup>2</sup> -7szt       |                       |
| 52m <sup>2</sup> -63m <sup>2</sup> -7szt                        |                       |
| 73m <sup>2</sup> -88m <sup>2</sup> -2szt                        |                       |