


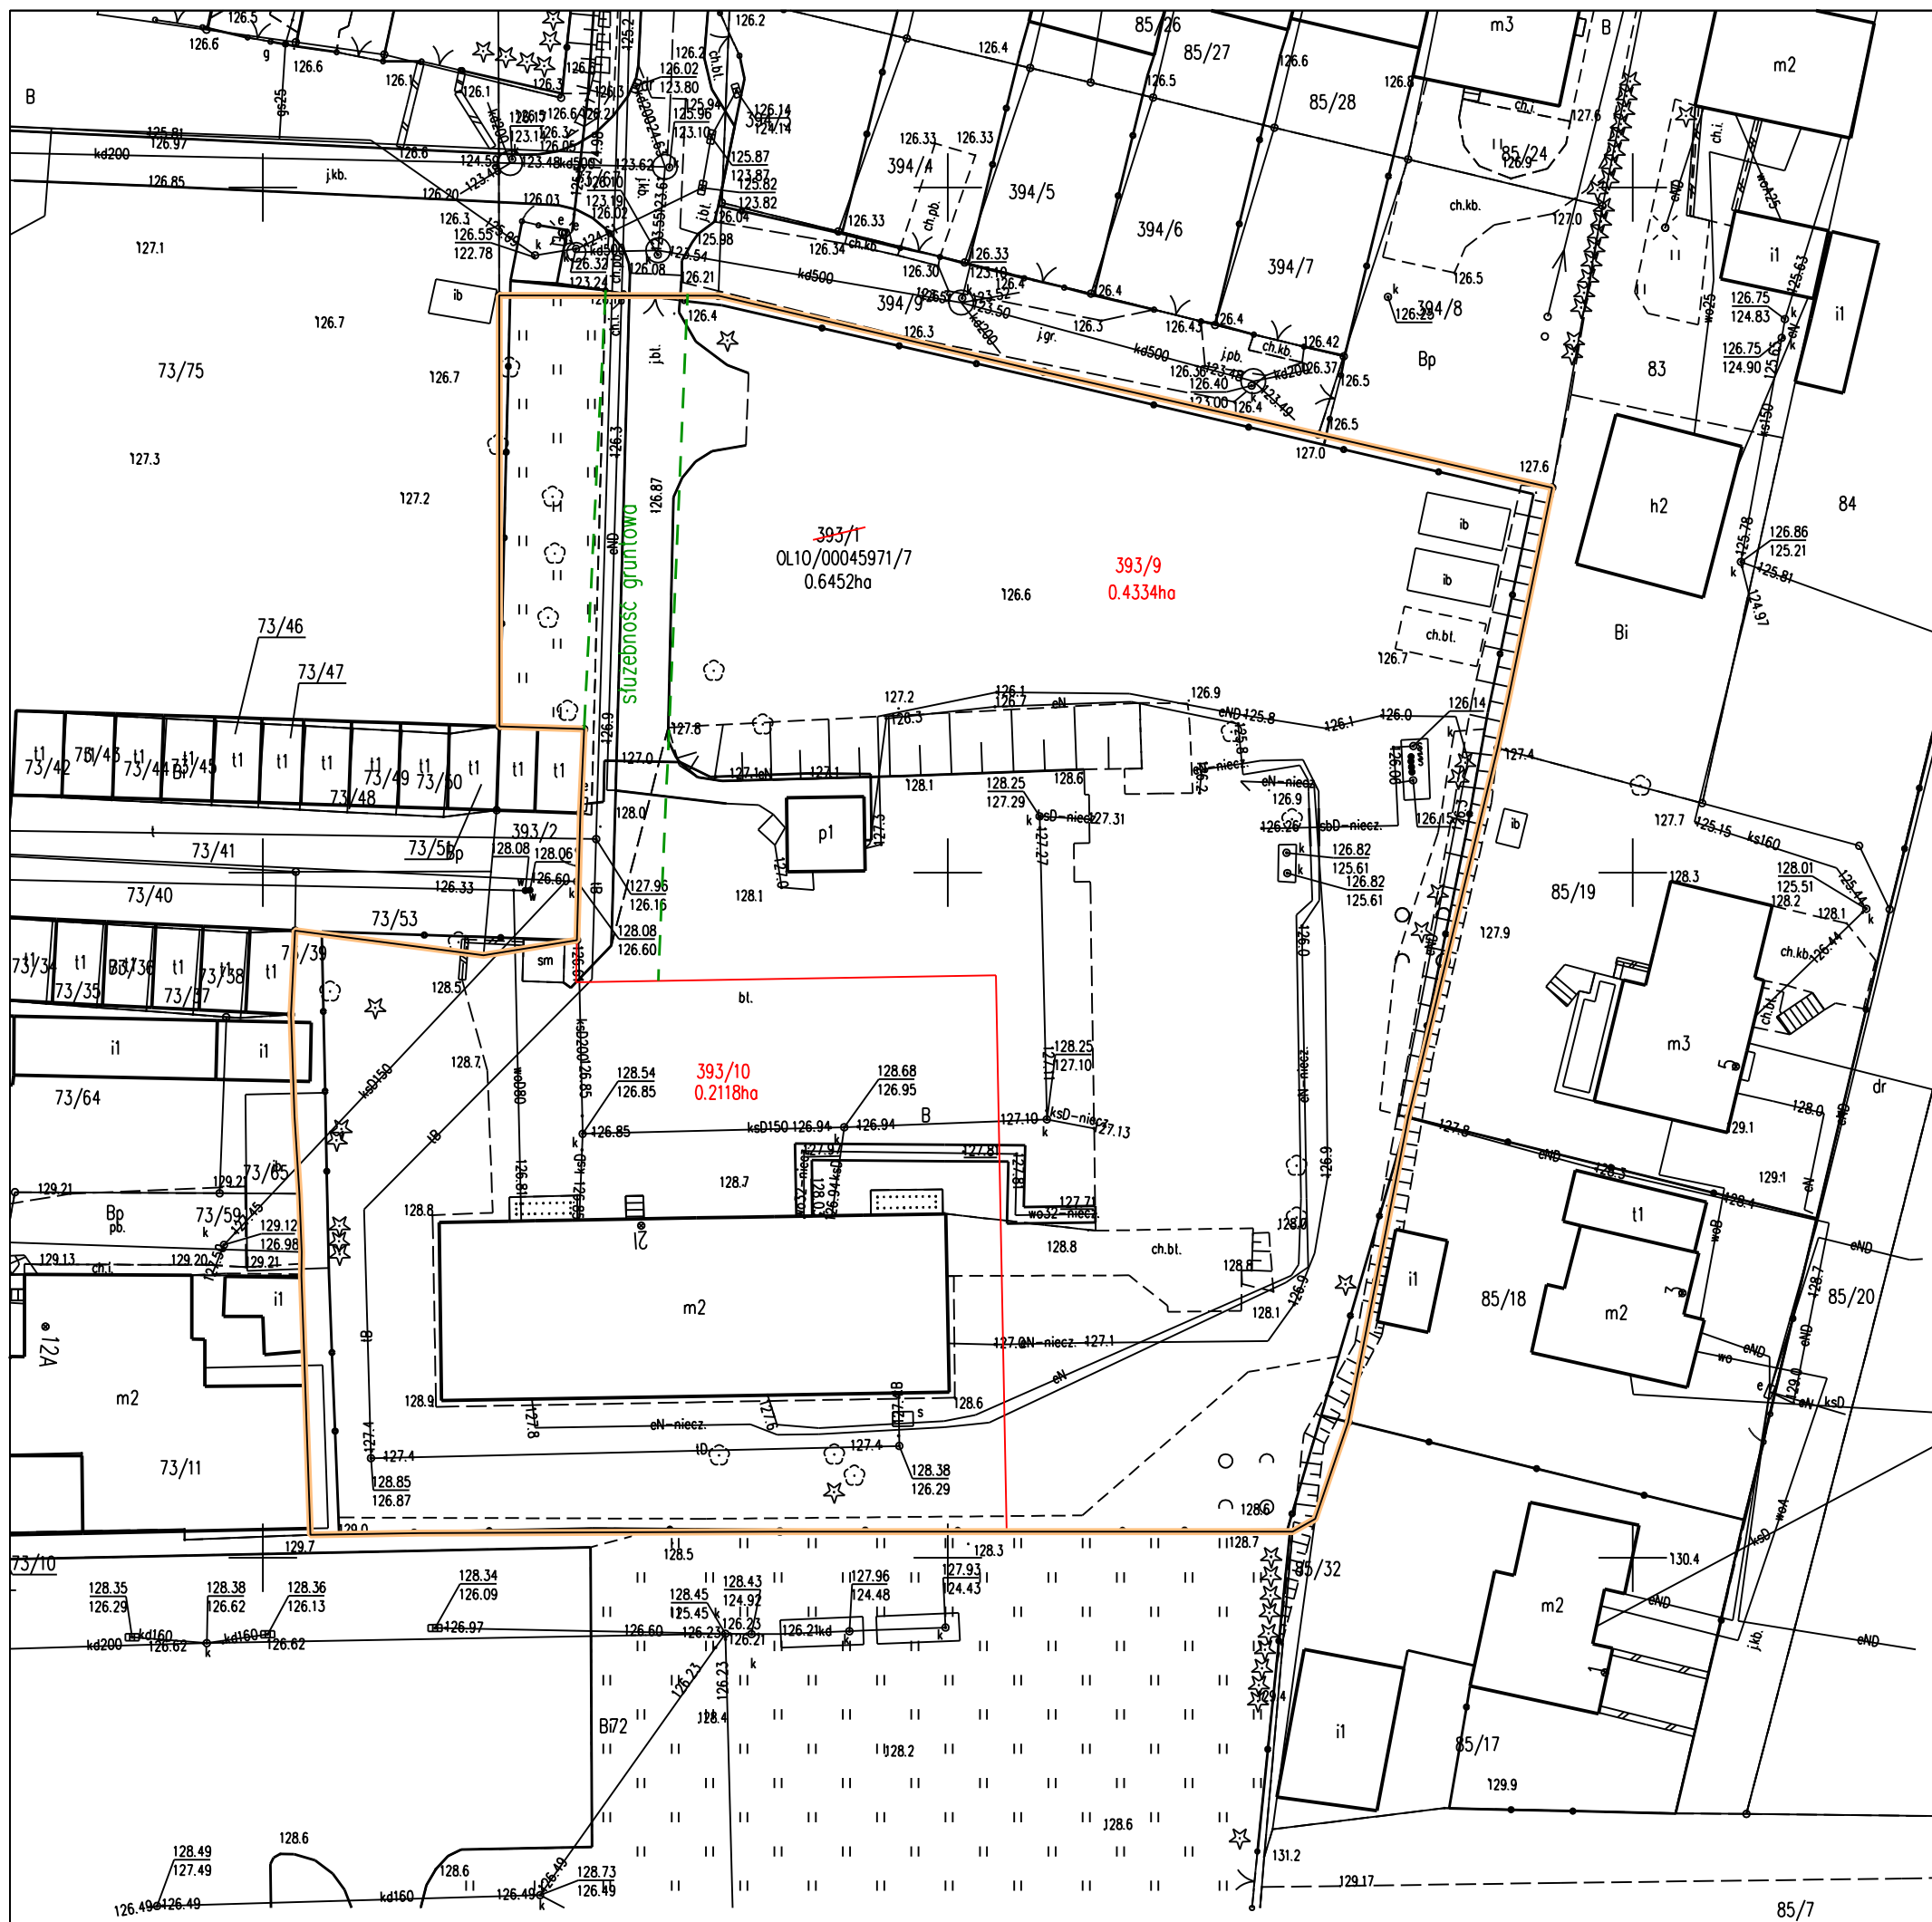

WSTĘPNY PROJEKT PODZIAŁU MAPA ZASADNICZA SKALA 1:500

Nr. zgł: GD-I.6642.1.2172.2026
Województwo : Warmińsko-Mazurskie
Powiat : olsztyński
Gmina : 281401 4 Miasto Barczewo
Obręb: 281401 4.0002 Miasto Barczewo 2
Arkusz : 7.209.18.18.1.2, 7.209.18.18.1.4
Działka: 393/1