


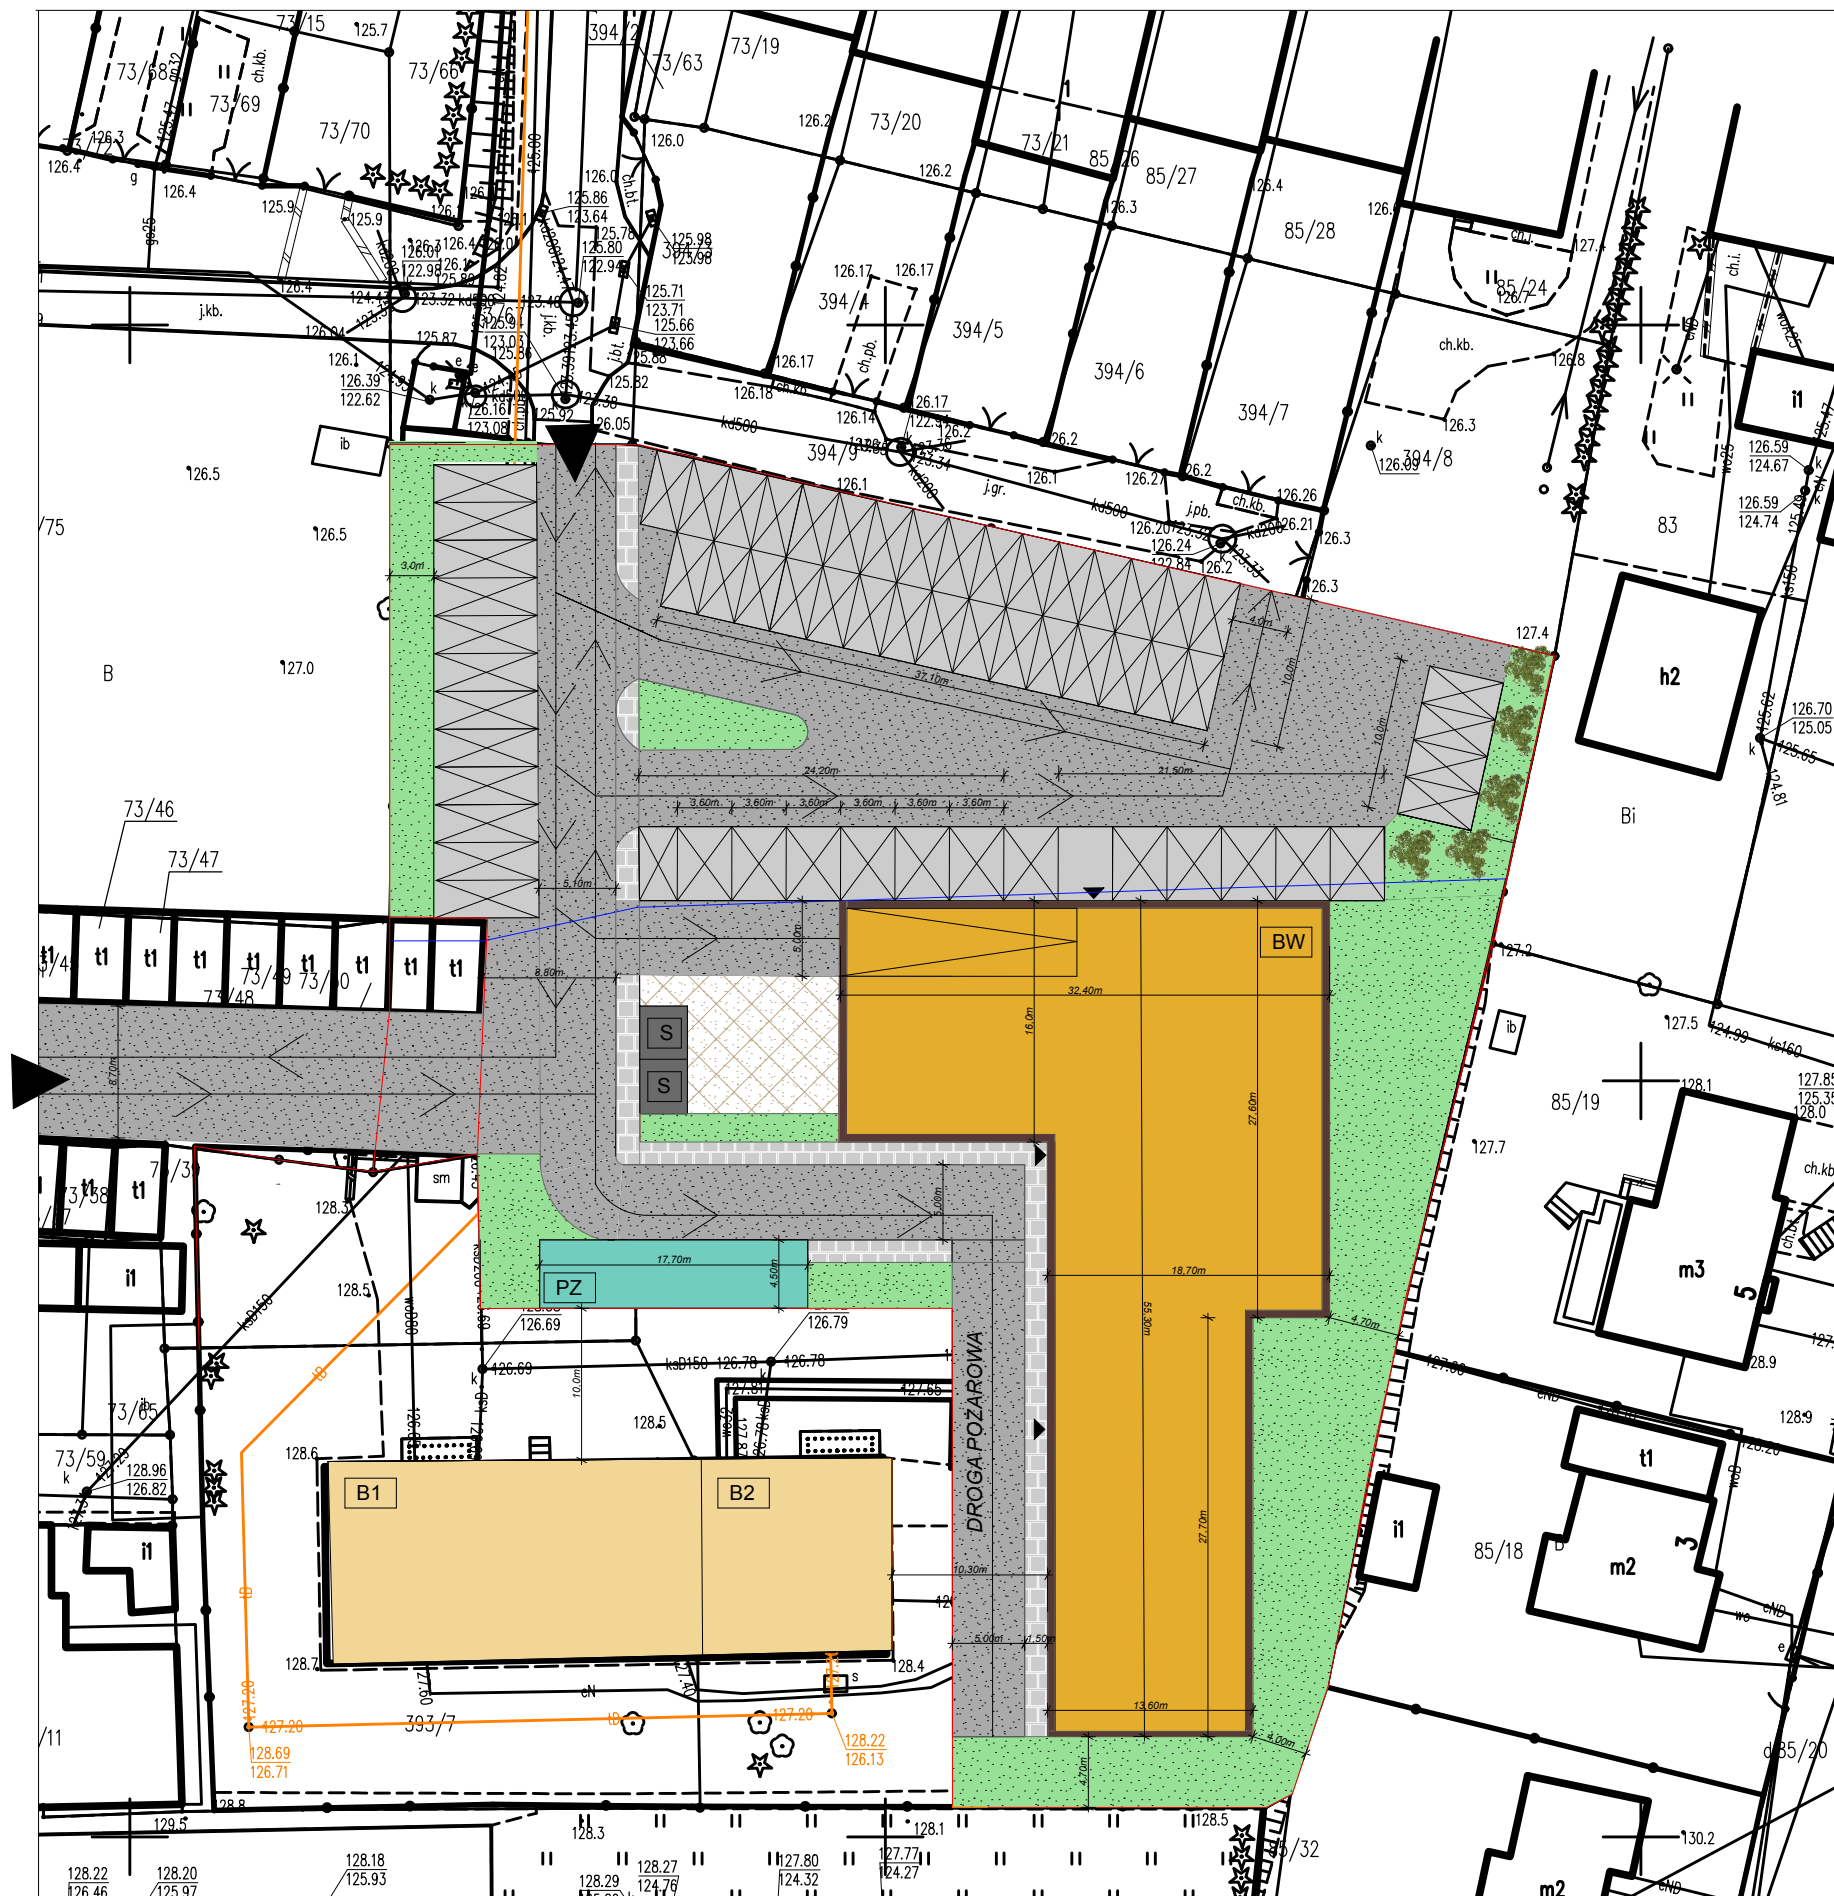

KONCEPCJA ZAGOSPODAROWANIA TERENU	
	ZAKRES INWESTYCJI
	LINIA ROZGRANICZAJĄCA TERENY MPZP
	PROJEKTOWANY BUDYNEK WIELORODZINNY 5-KONDYGNACYJNY+GARAŻ PODZIEMNY
	ISTNIEJĄCE BUDYNKI WIELORODZINNE
	PLAC ZABAW, TEREN REKREACYJNY
	LOKALIZACJA ŚMIETNIKA
	POWIERZCHNIA BIOLOGICZNIE CZYNNNA
	DOJAZDY-KOMUNIKACJA KOŁOWA
	MIEJSCA POSTOJOWE-PARKINGI
	DOJŚCIA-KOMUNIKACJA PIESZA
	TEREN WYŁĄCZONY
	WJAZD NA DZIAŁKĘ
	PROJEKTOWANA ZIELEŃ
	WEJŚCIA DO BUDYNKU
MIEJSCA POSTOJOWE:	
ILOŚĆ MIEJSC POSTOJOWYCH W TERENIE: 60SZT	
W TYM:	
-12 MIEJSC POSTOJOWYCH DLA OSÓB Z NIEPEŁNOSPRAWNOŚCIĄ	
ILOŚĆ MIEJSC POSTOJOWYCH W GARAŻU PODZIEMNYM : 41SZT	
W TYM:	
-4 MIEJSCA POSTOJOWE DLA OSÓB Z NIEPEŁNOSPRAWNOŚCIĄ	
<u>SUMA: 101 MIEJSC POSTOJOWYCH</u>	
BILANS POWIERZCHNI:	
•POWIERZCHNIA CZĘŚCI DZIAŁKI 393/1 (WPZ 0,25)	4472,00m ²
•POWIERZCHNIA ZABUDOWY	1112,04 m ²
•POWIERZCHNIA BIOLOGICZNIE CZYNNNA (15%)	678,63m ²
•POWIERZCHNIA UTWARDZONA	2659,33m ²
•POWIERZCHNIA PLACU ZABAW	22,20m ²

KONCEPCJA ZAGOSPODAROWANIA BARCZEWO dz.nr 393/1, obr.2, m. Barczewo.